




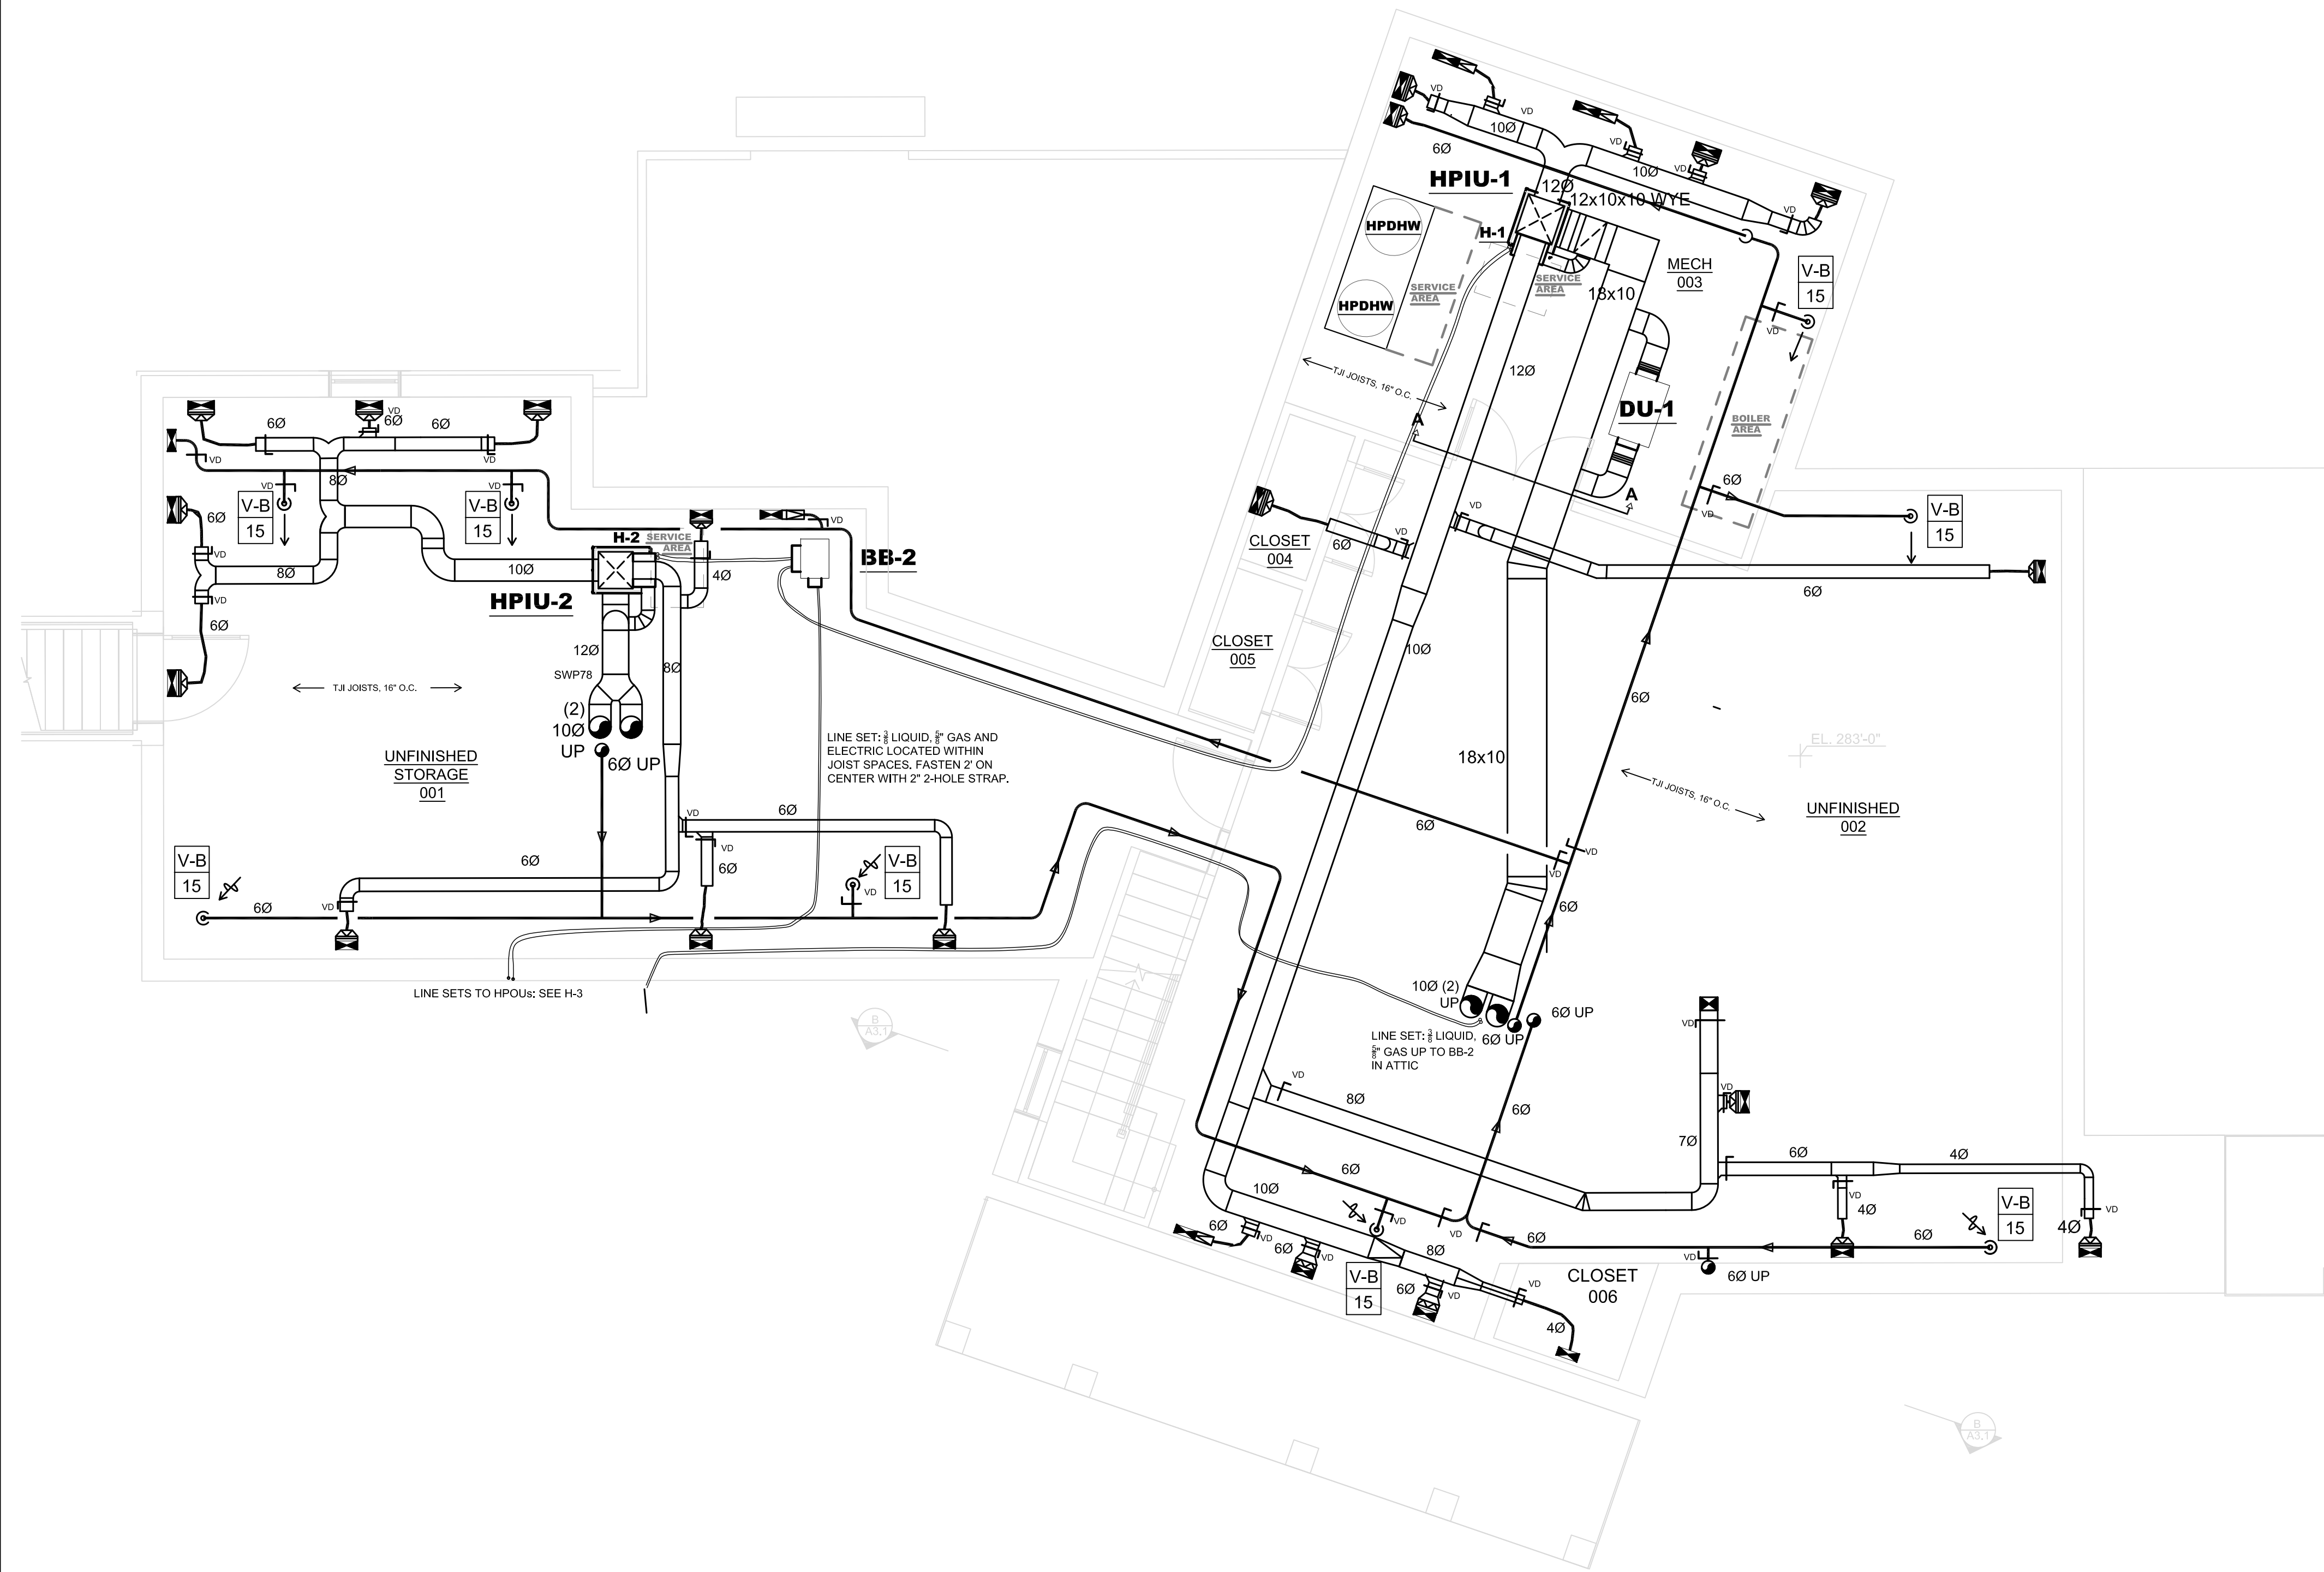

BASEMENT PLAN
SCALE: $\frac{1}{4} = 1'0''$

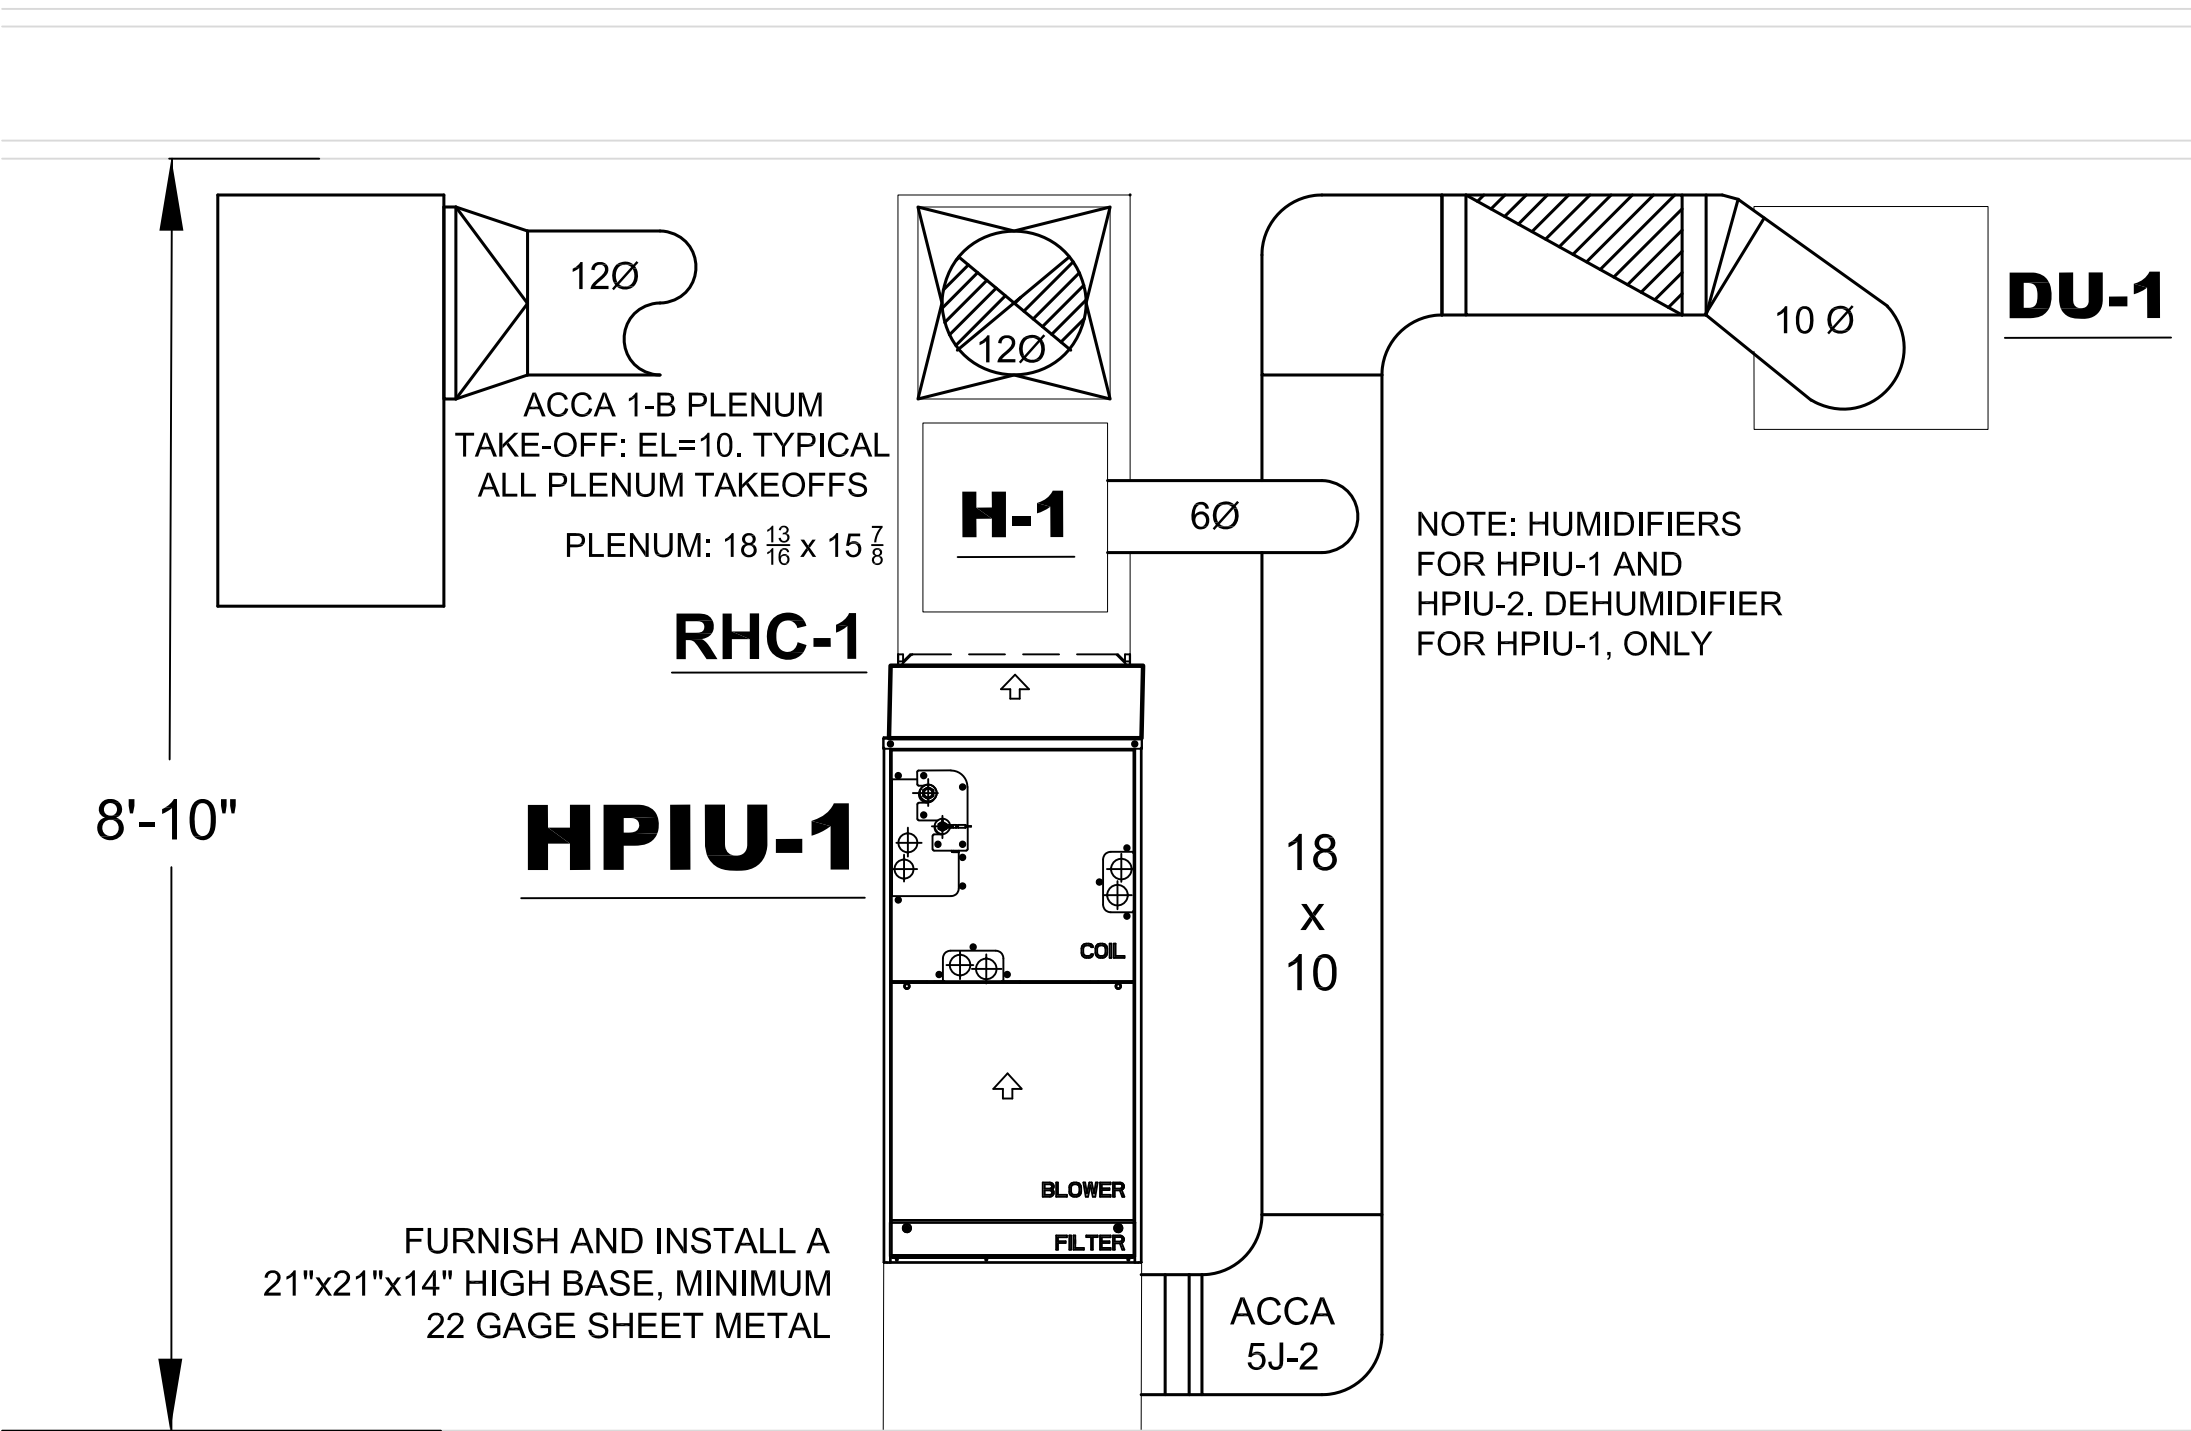

SECTION A-A
SCALE: $\frac{3}{4} = 1'0''$

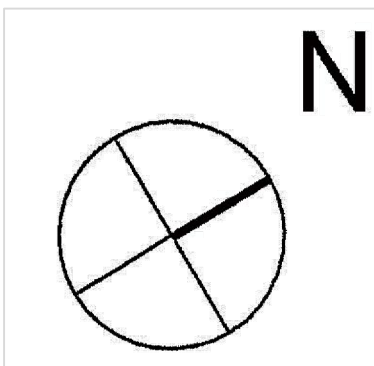

PROGRESS	
<i>General Contractor</i> RON DUNN BUILDERS Farmington, ME https://dunnbuilders.net 207-314-3911	
<i>HVAC Design</i> OCTOBER ENGINEERING LLC Palermo, ME; Sudbury, MA https://octoberengineering.com 207-649-0505; 508-561-7553	
<i>Owners</i> RICHARD & WENDY HAENSSLER Chelmsford, MA 973-220-8069	
RESIDENCE PARKHILL POINT ROAD BELGRADE, ME 04917	
HVAC LOWER LEVEL	
02-14-24	H-2 2 of 6