


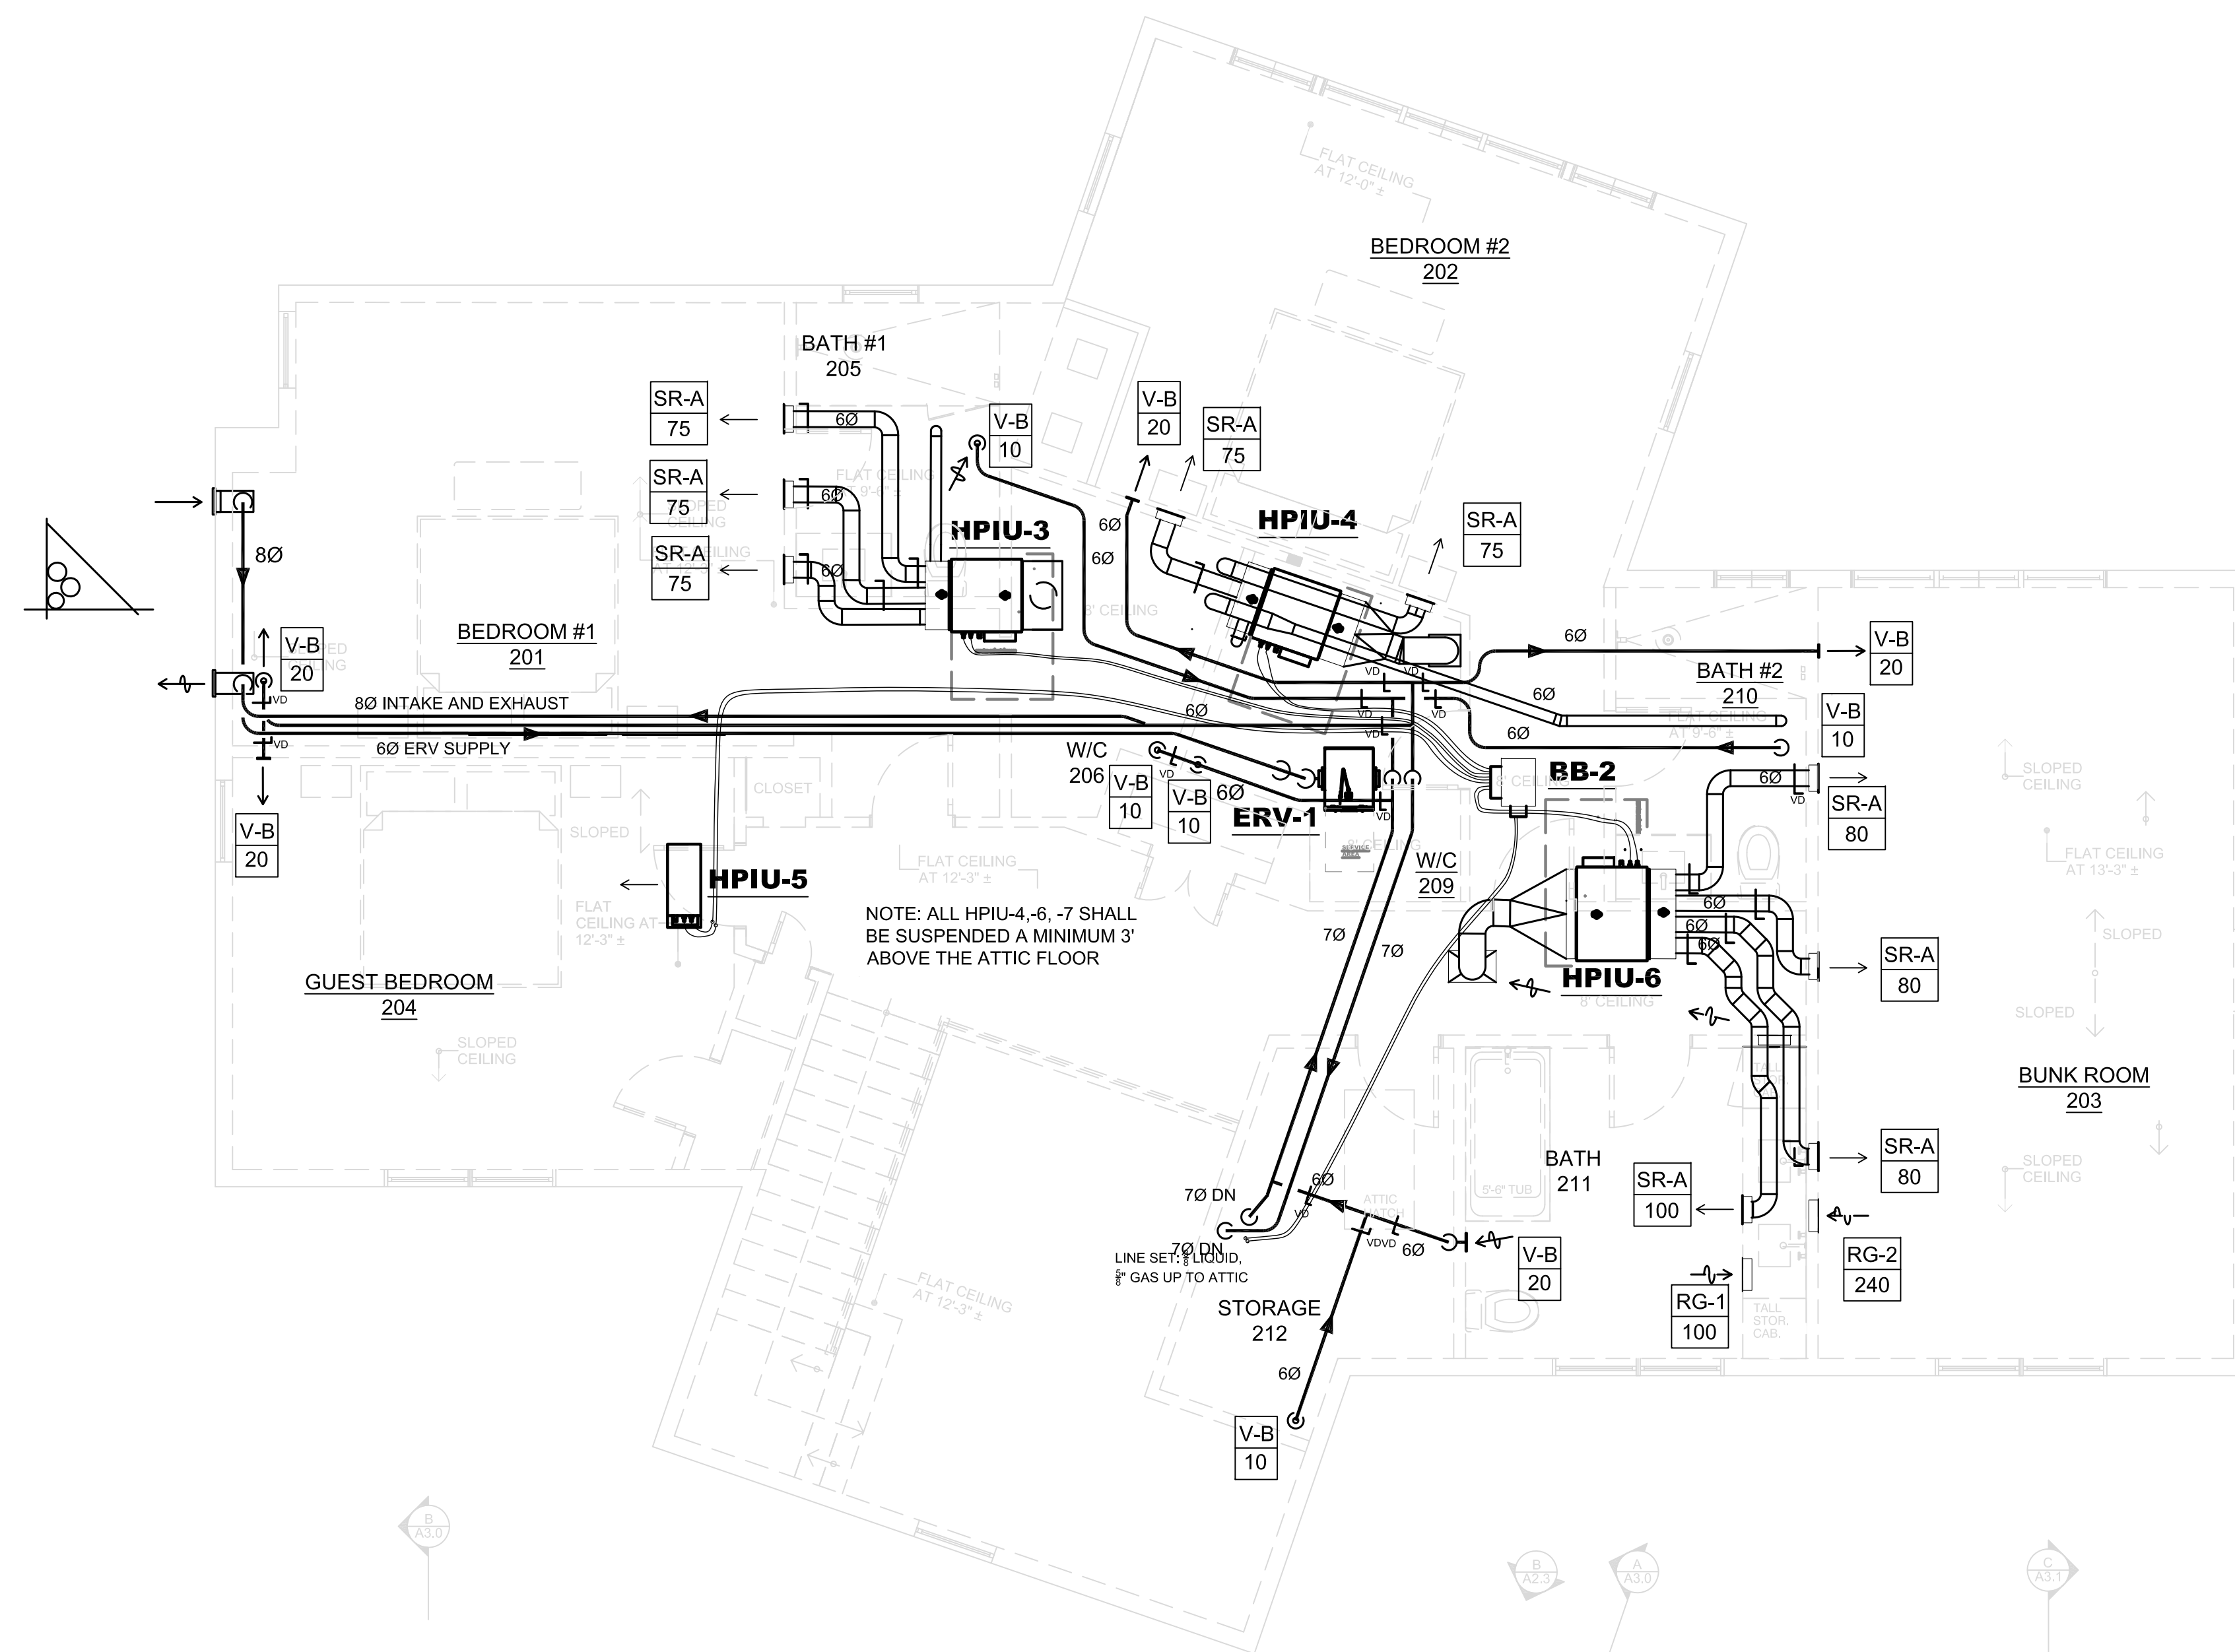

ATTIC FLOOR PLAN

SCALE: $\frac{1}{4}" = 1'0"$

PROGRESS

General Contractor
RON DUNN BUILDERS
Farmington, ME
<https://dunnbuilders.net>
207-314-3911

HVAC Design
OCTOBER ENGINEERING LLC
Palermo, ME; Sudbury, MA
<https://octoberengineering.com>
207-649-0505; 508-561-7553

Owners
RICHARD & WENDY HAENSSLER
Chelmsford, MA
973-220-8069

RESIDENCE
PARKHILL POINT ROAD
BELGRADE, ME 04917

HVAC
ATTIC FLOOR

02-14-24

H-5
5 of 6

