



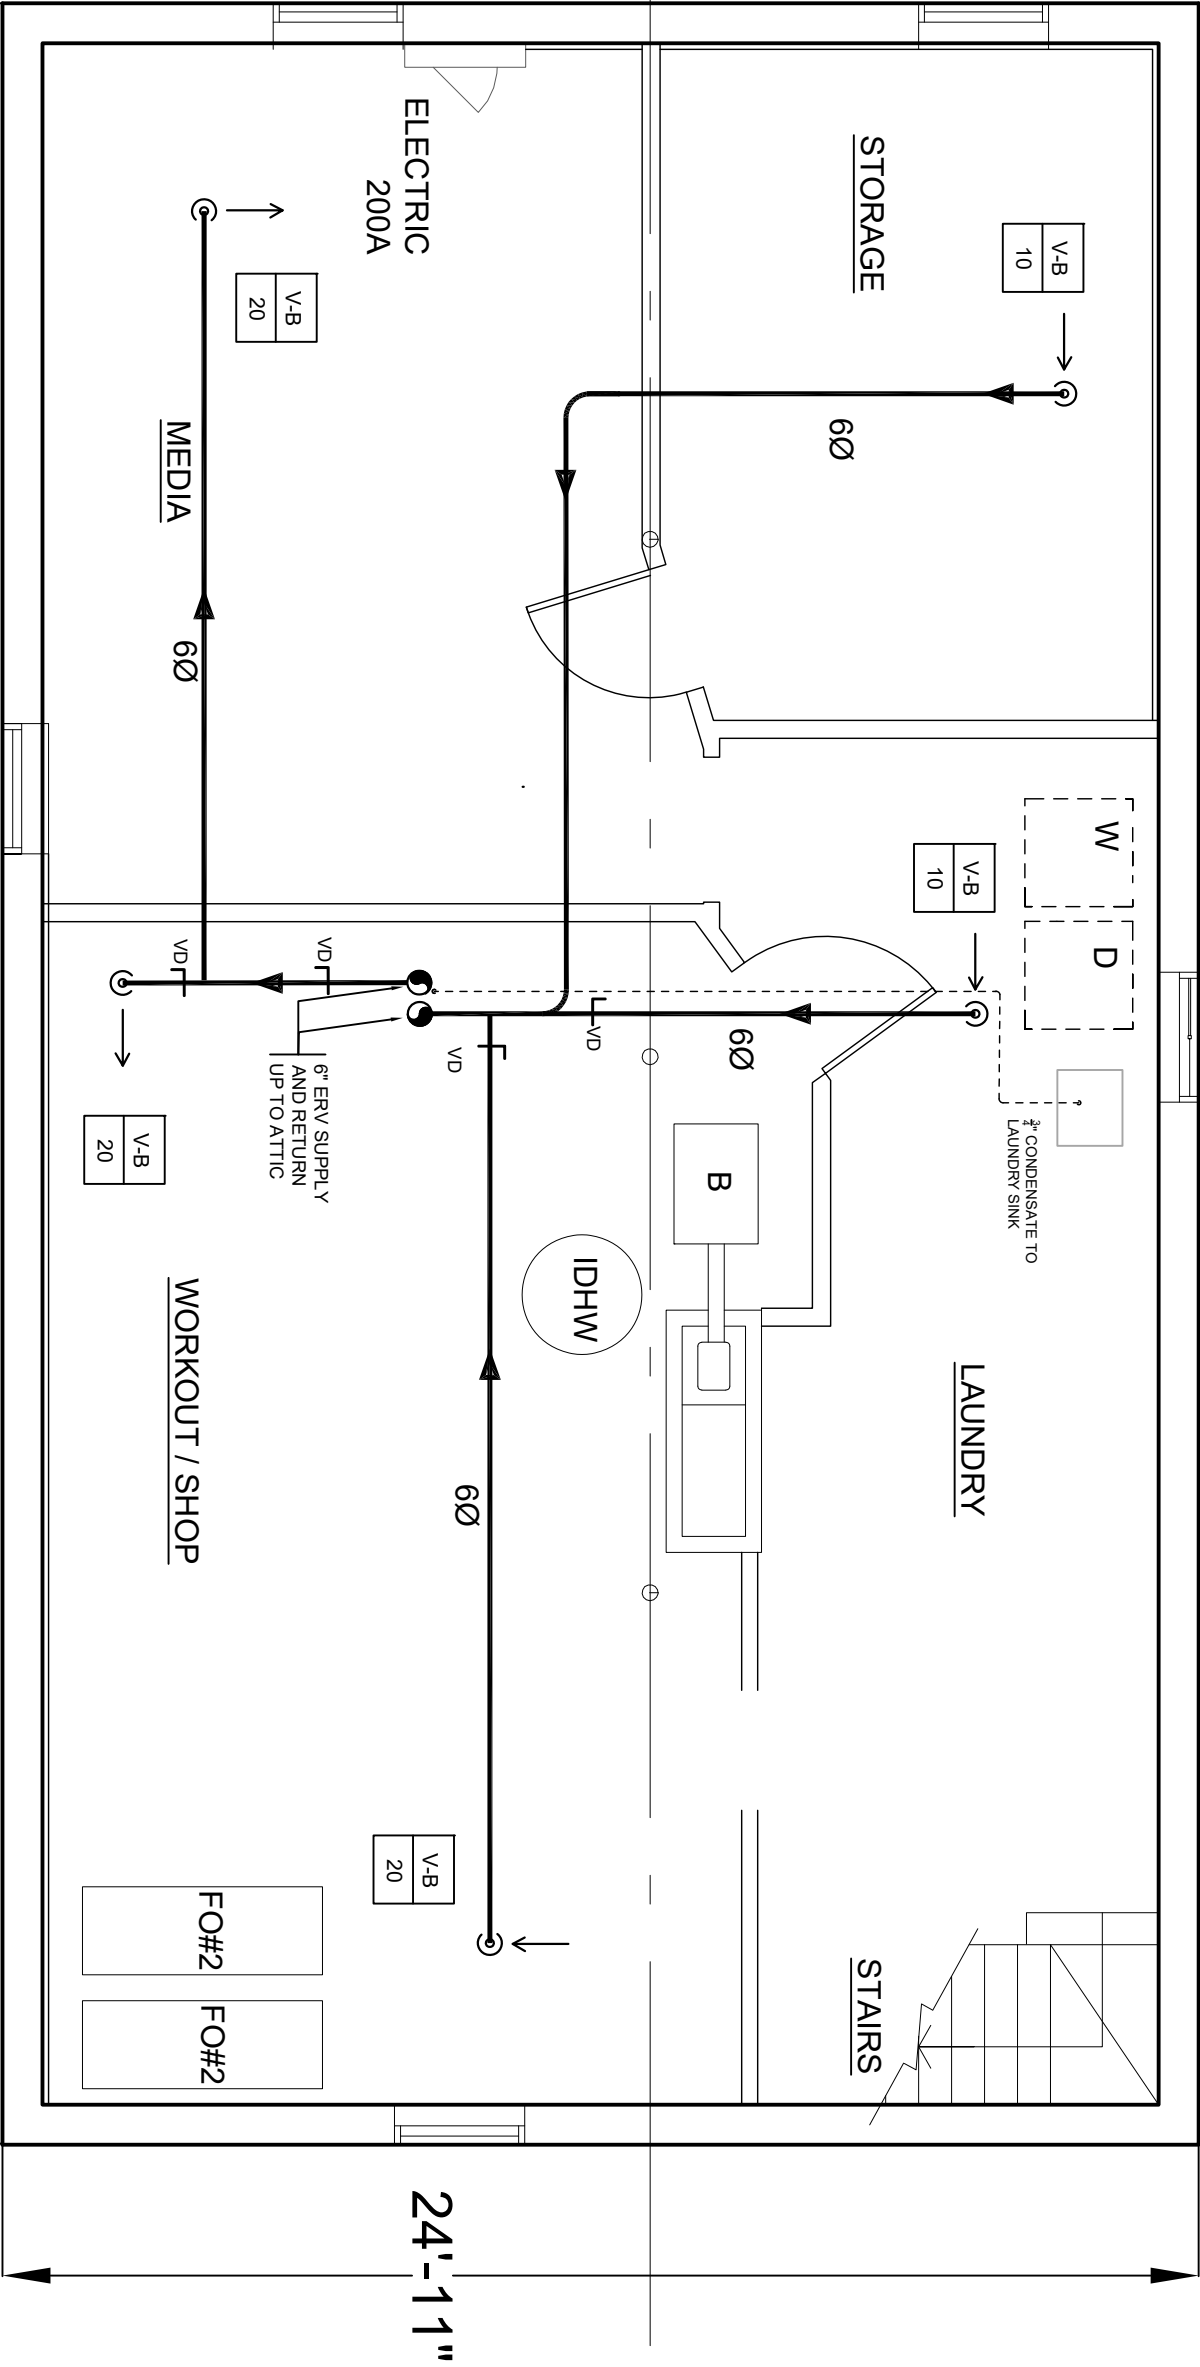


44'-7"

24'-11"

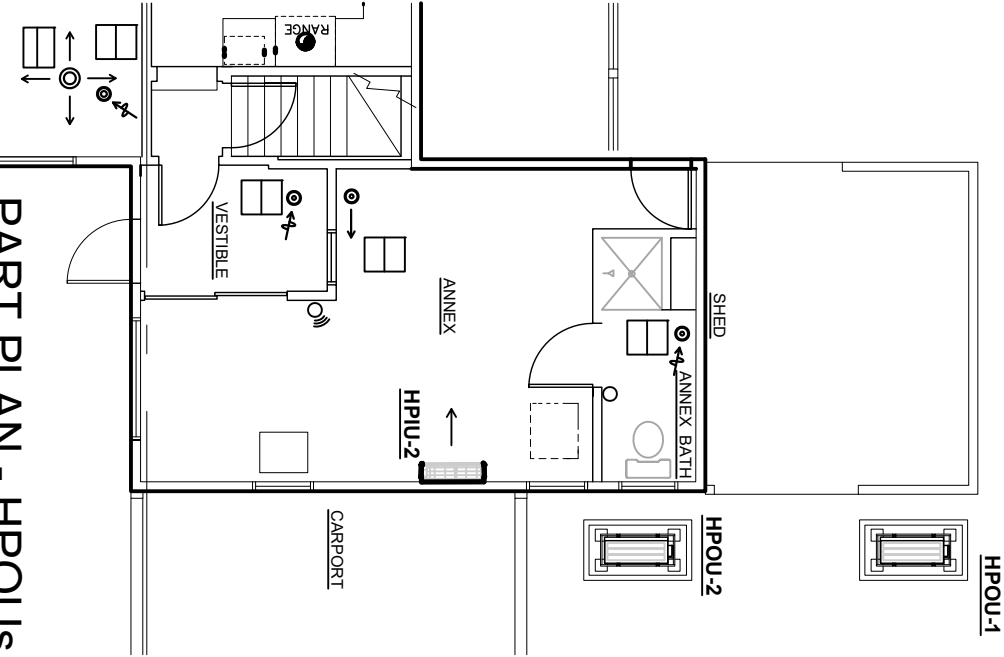

SCALE: $\frac{1}{8}$ " = 1'0" (11x17)

PART PLAN - HPOUS

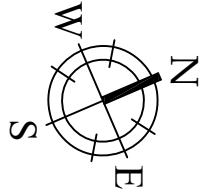

Owners Vander Straeten, Ghosh Wayland, MA	
HVAC Design OCTOBER ENGINEERING LLC Sudbury, MA 01776 508-561-7553	
ENERGY RETROFIT AND ELECTRIFICATION 13 Rice Spring Lane Wayland, MA 01778	
HVAC BASEMENT	
10-10-2025	H-3 3 of 5