


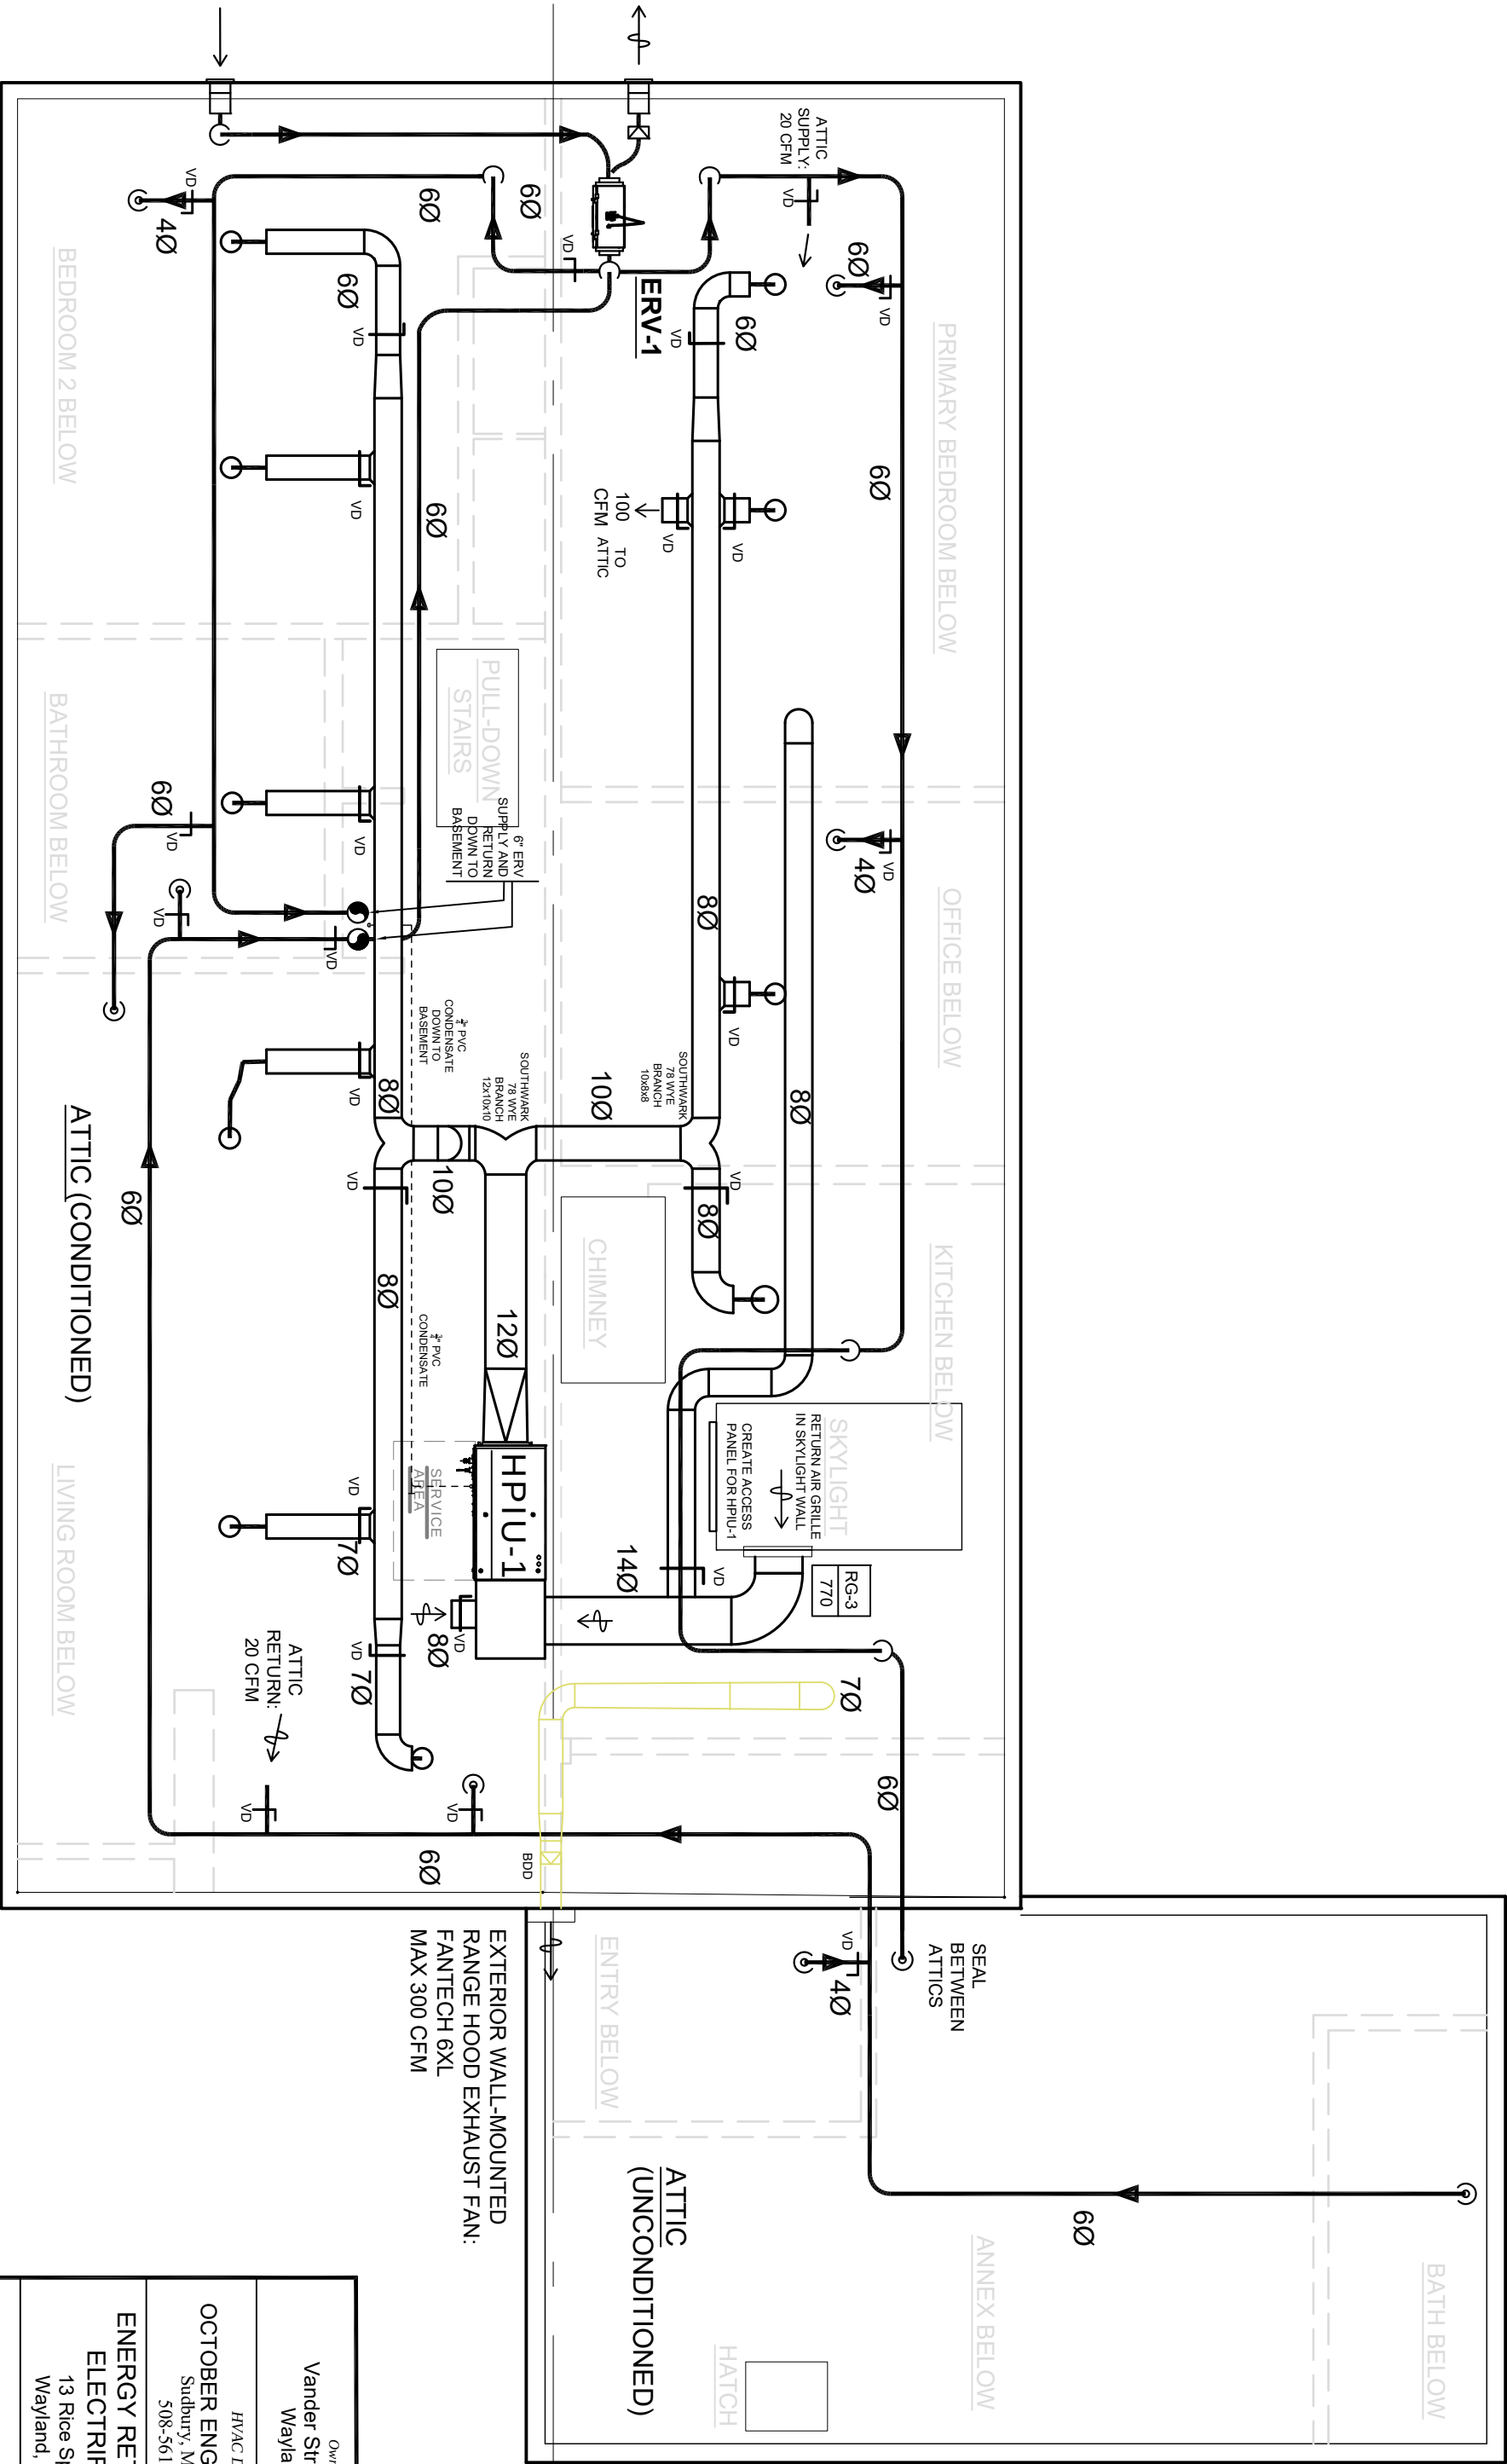

ATTIC PLAN

SCALE: 1/4" = 1'0" (11x17)

Owners Vander Straeten, Ghosh Wayland, MA	
HVAC Design OCTOBER ENGINEERING LLC Sudbury, MA 01776 508-561-7553	
ENERGY RETROFIT AND ELECTRIFICATION 13 Rice Spring Lane Wayland, MA 01778	
HVAC ATTIC	
10-10-2025	H-5 5 of 5