



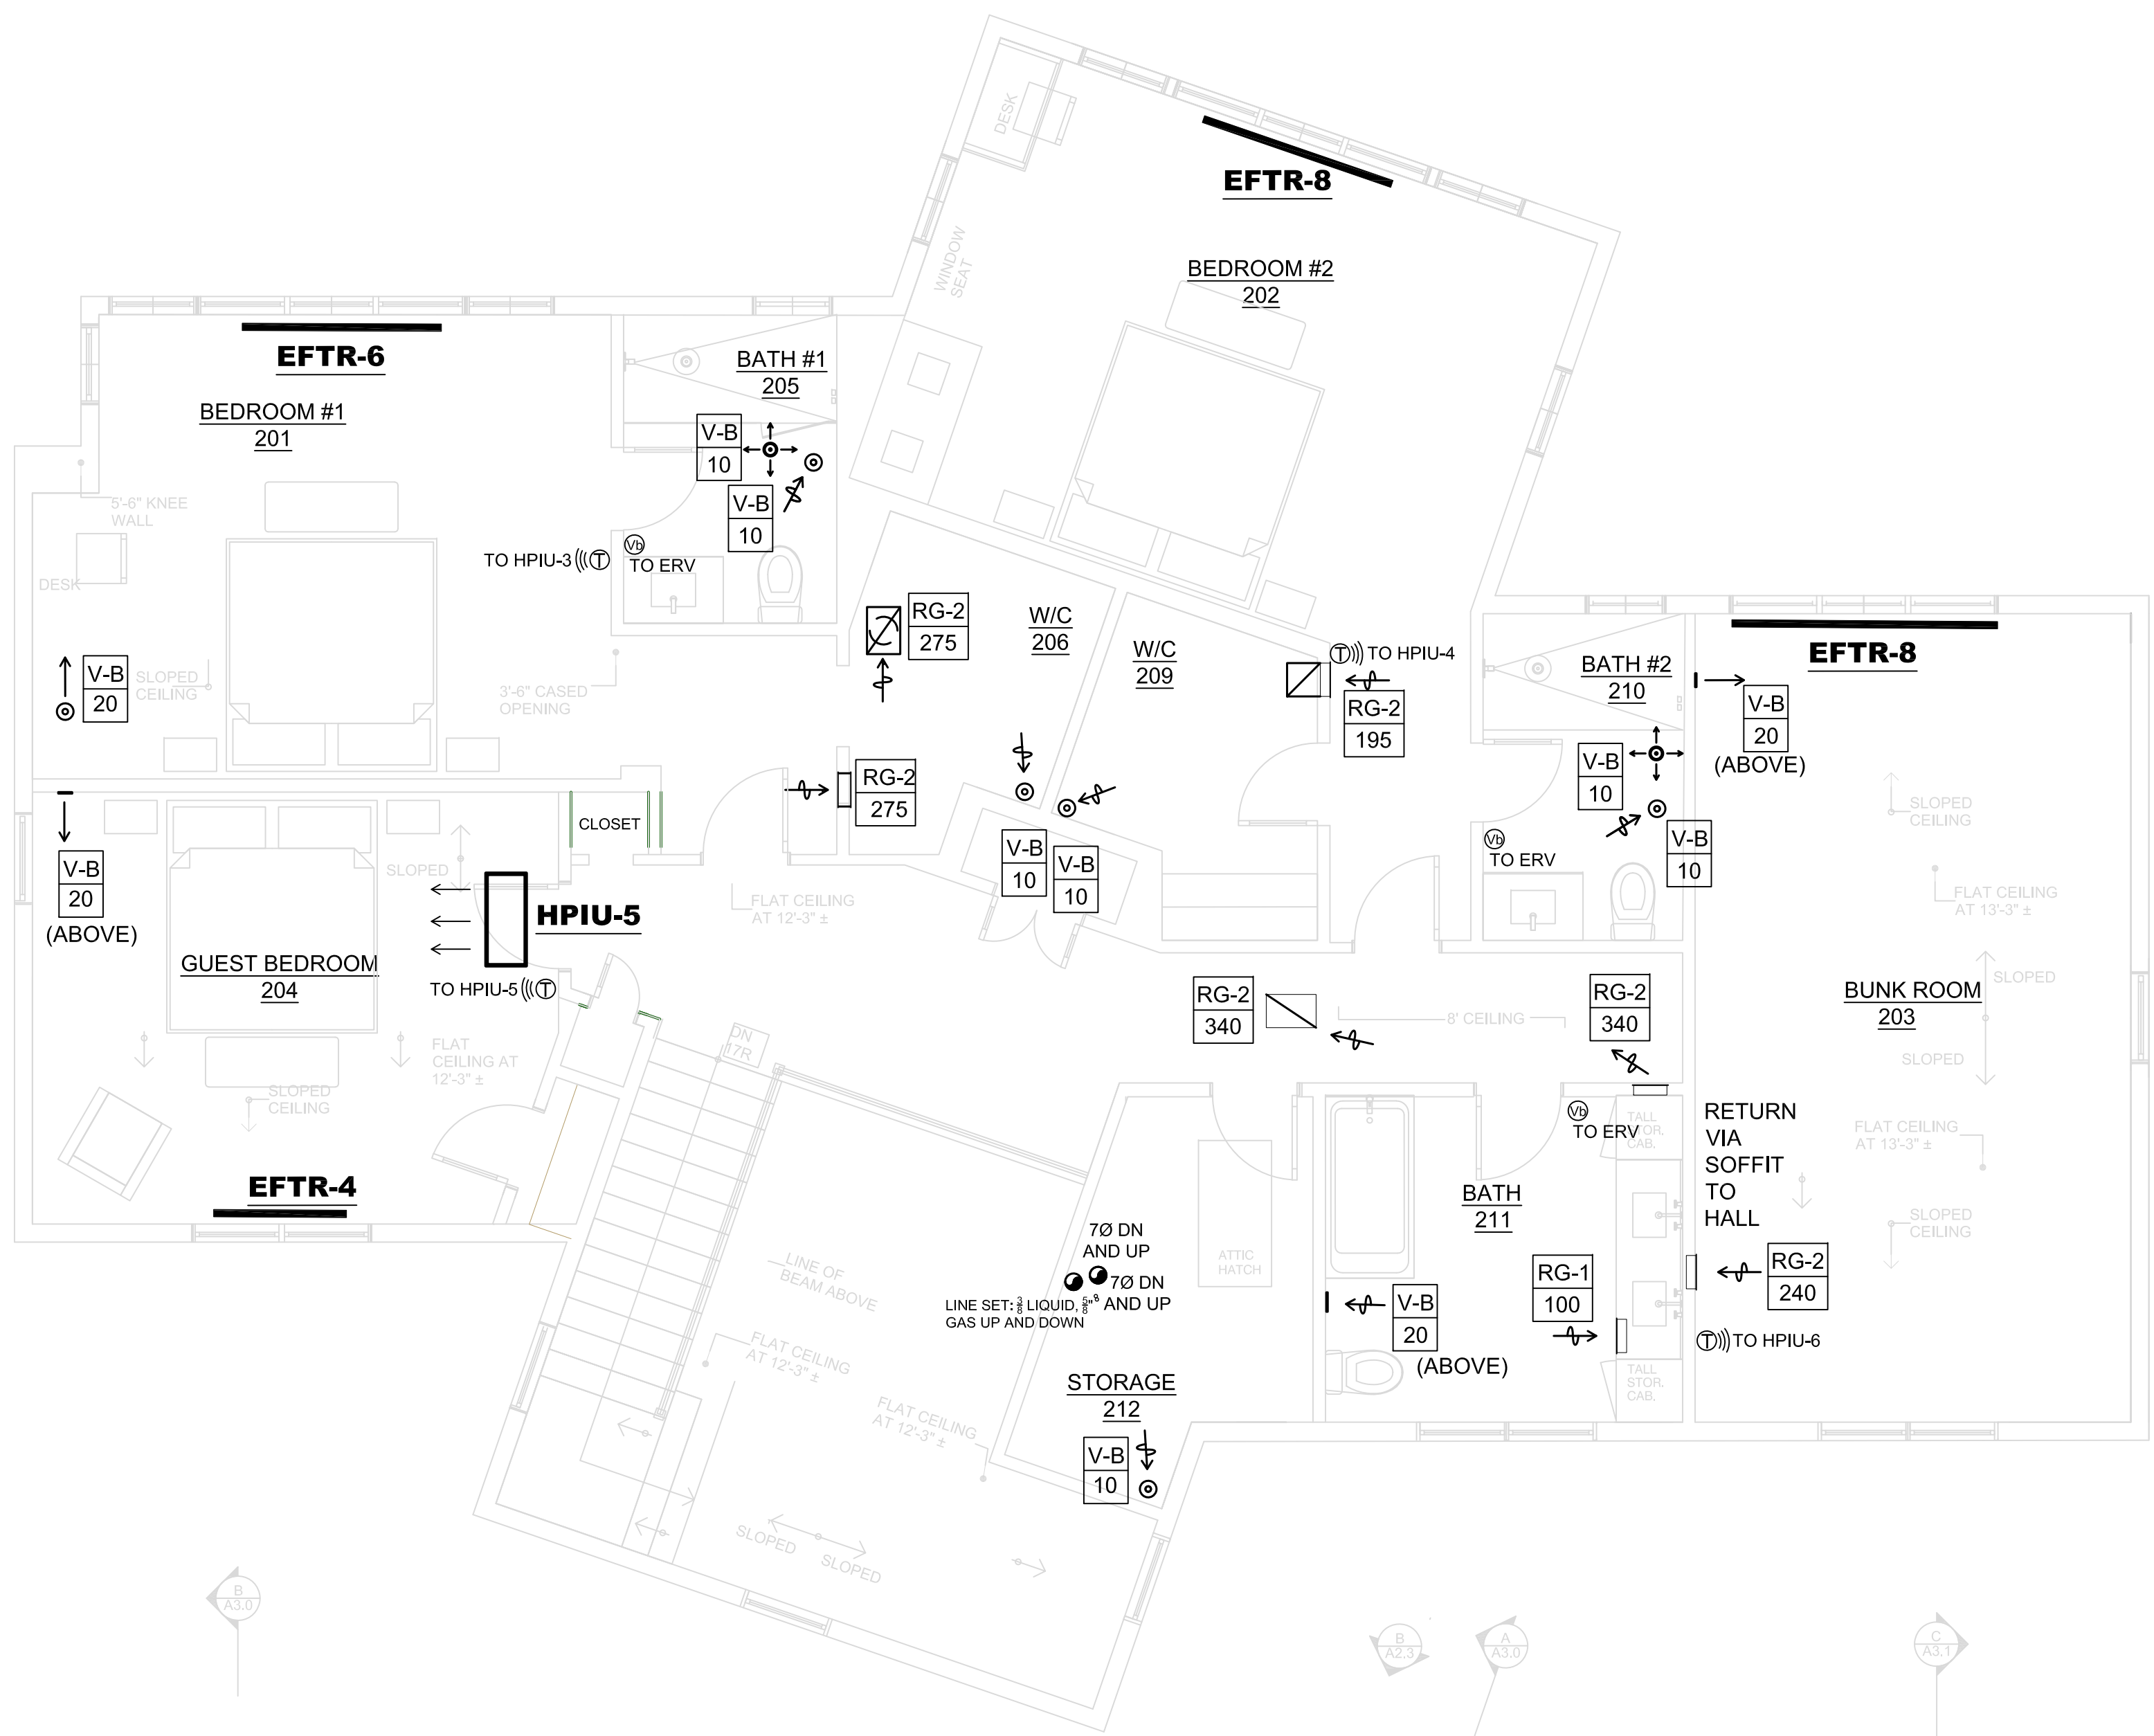

SECOND FLOOR PLAN
SCALE: 1/4" = 1'0"

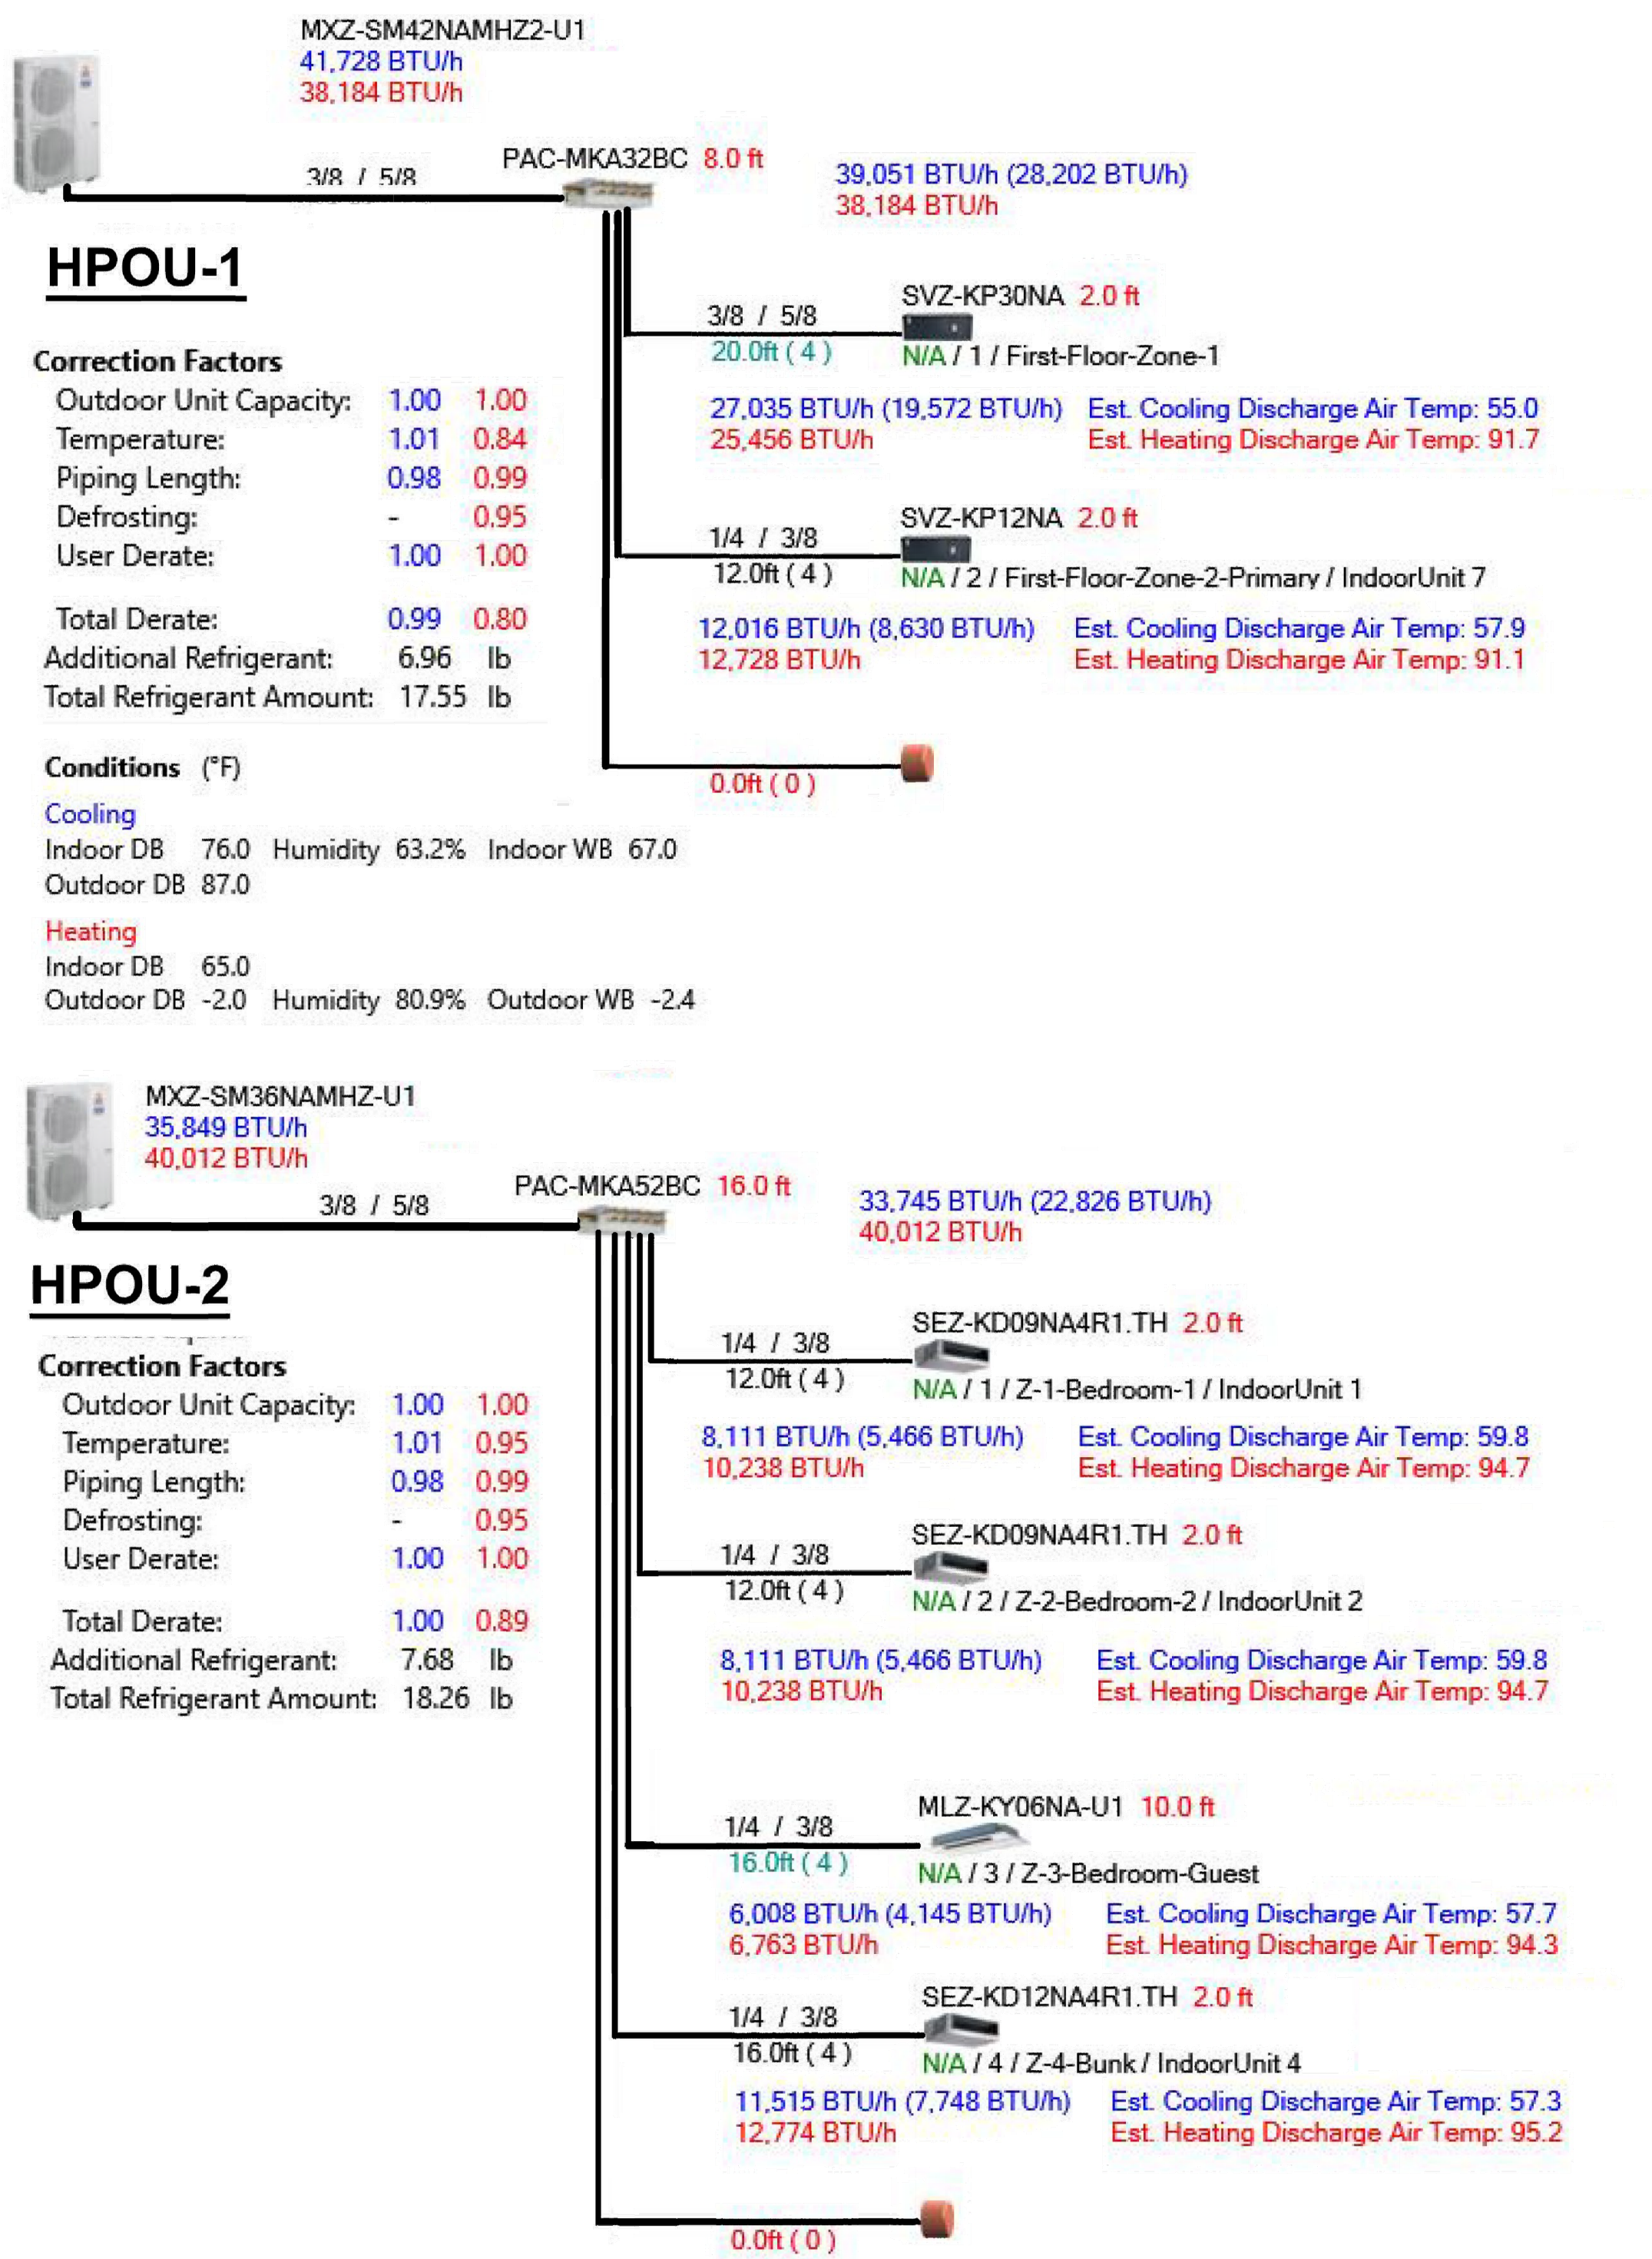

HEAT PUMP SYSTEM SCHEMATICS
SCALE: NONE

PROGRESS

General Contractor RON DUNN BUILDERS Farmington, ME https://dunnbuilders.net 207-314-3911	
HVAC Design OCTOBER ENGINEERING LLC Palermo, ME; Sudbury, MA https://octoberengineering.com 207-649-0505; 508-561-7553	
Owners RICHARD & WENDY HAENSSLER Chelmsford, MA 973-220-8069	
RESIDENCE PARKHILL POINT ROAD BELGRADE, ME 04917	
HVAC SECOND FLOOR	
02-14-24	H-4 4 of 6