



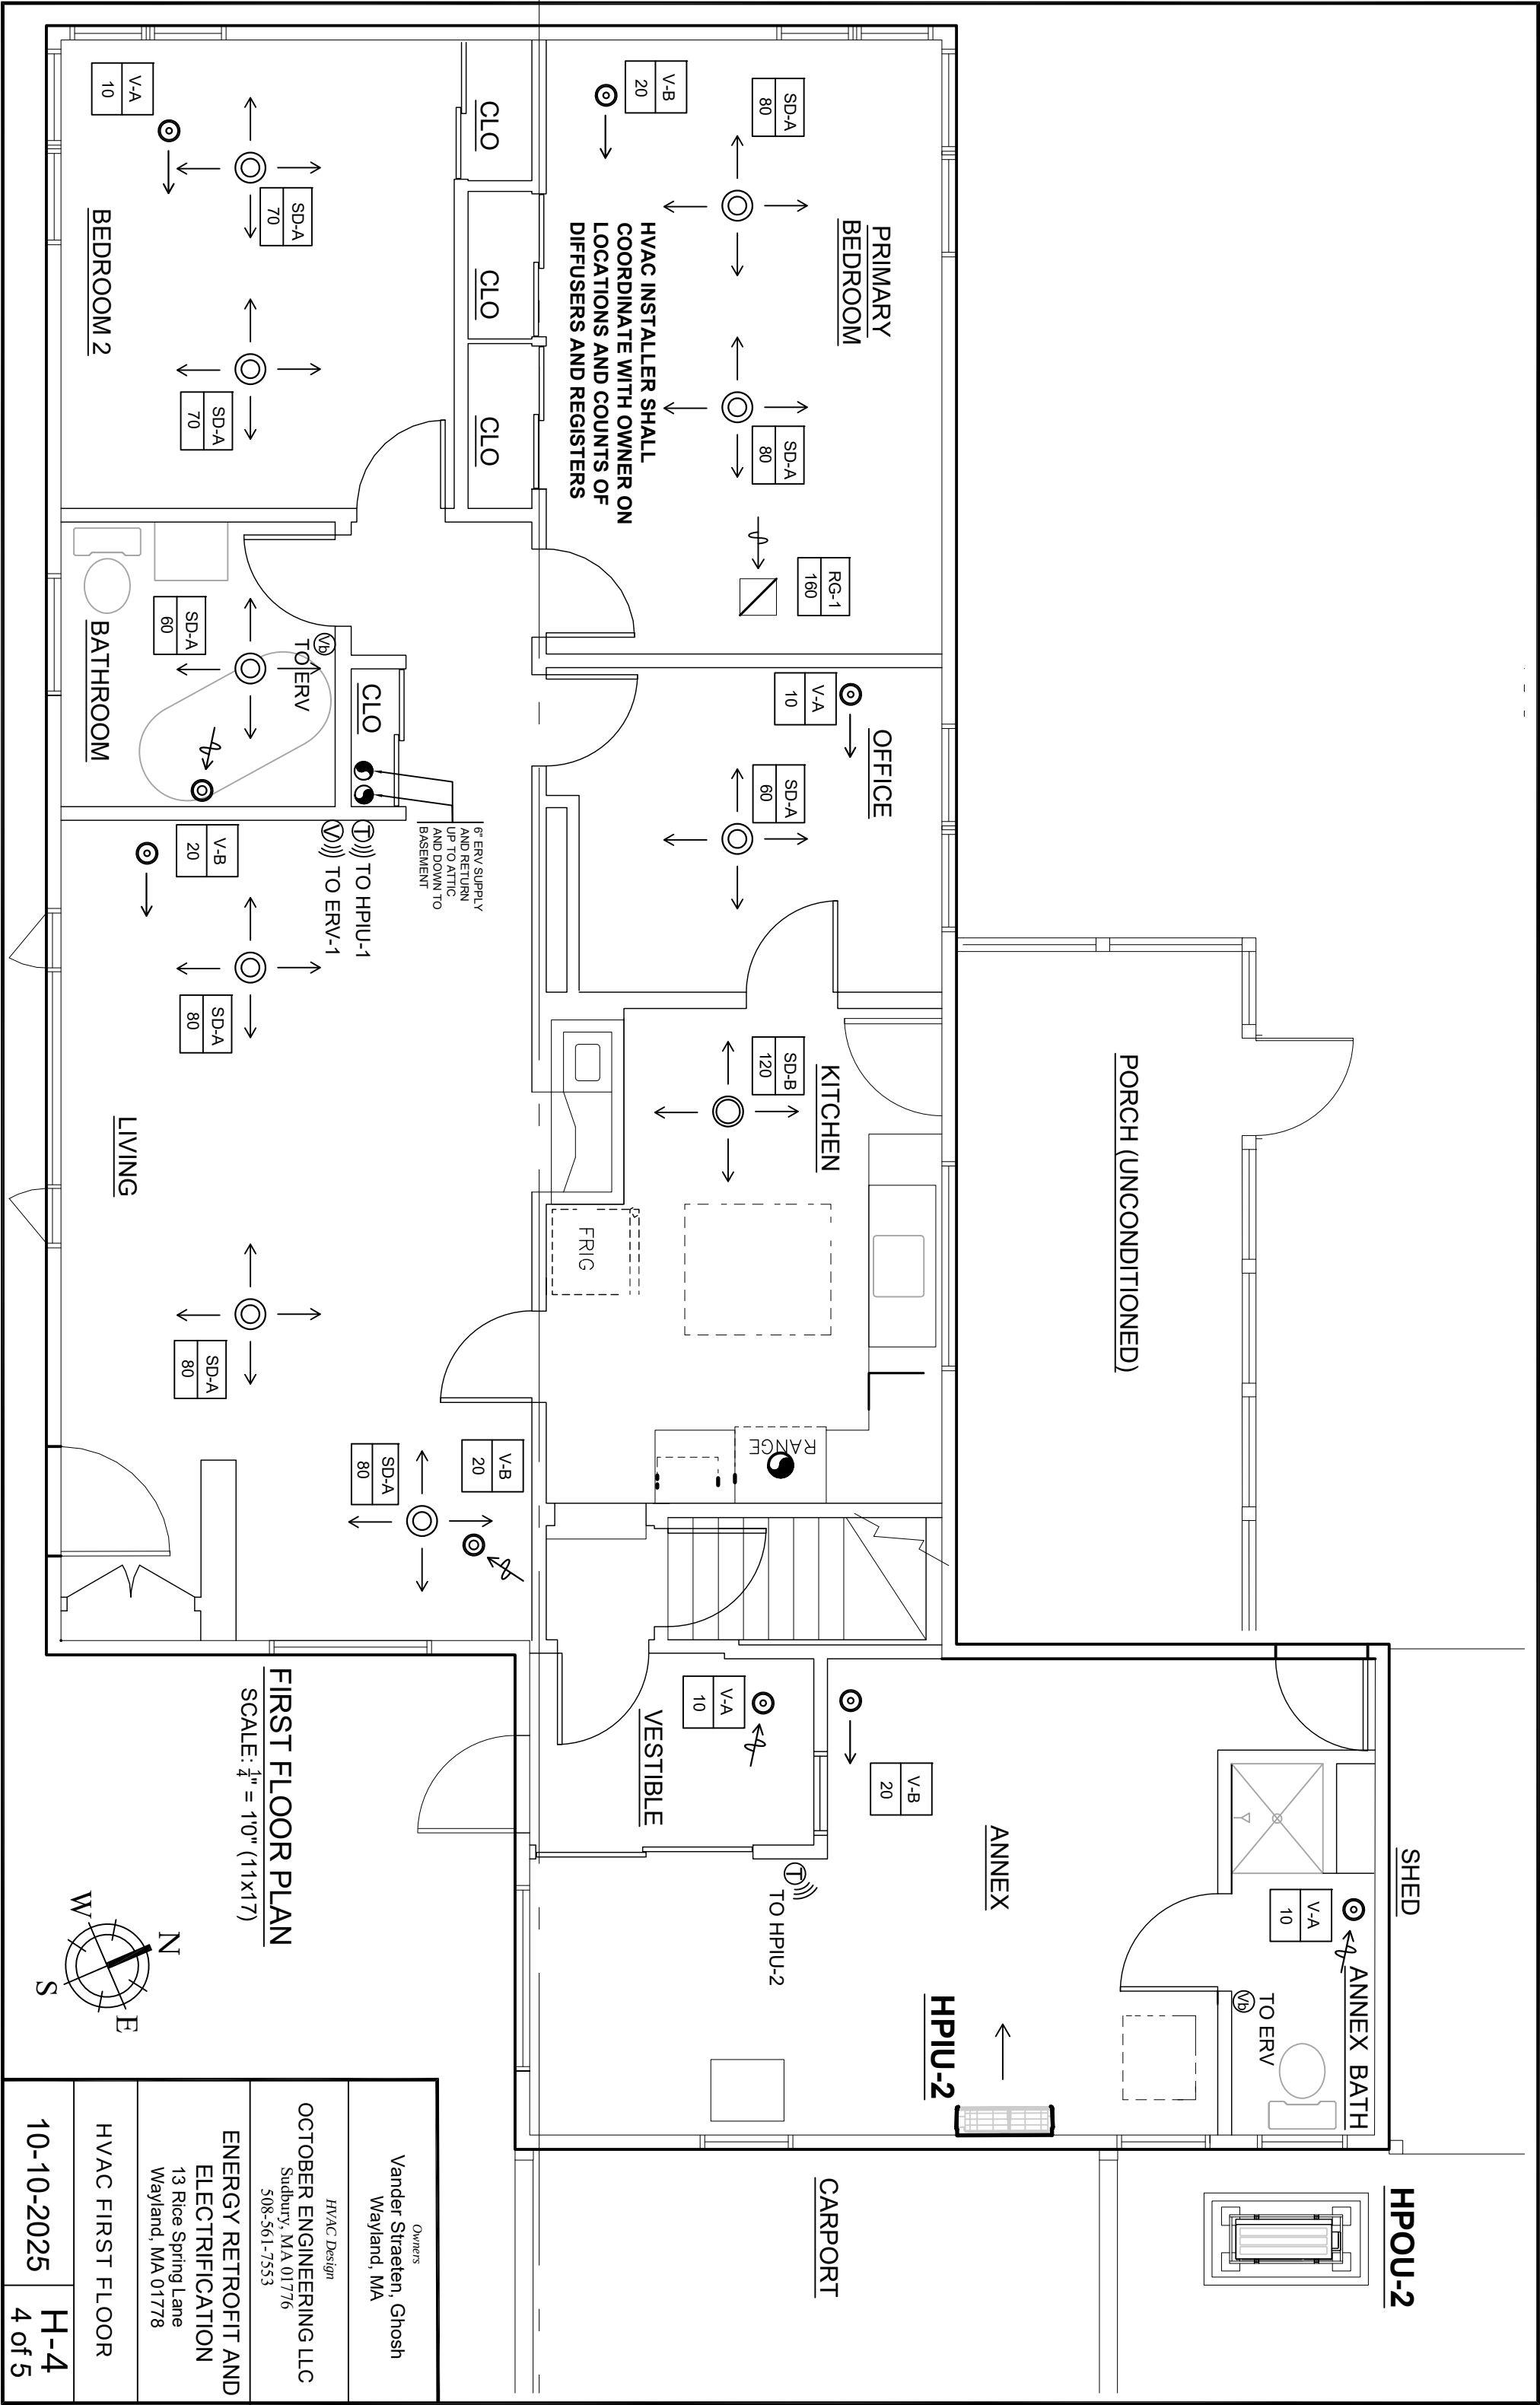

FIRST FLOOR PLAN
SCALE: 1/4" = 1'0" (11x17)

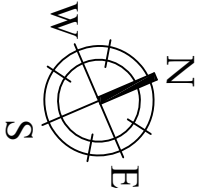

Owners Vander Straeten, Ghosh Wayland, MA	
HVAC Design OCTOBER ENGINEERING LLC Sudbury, MA 01776 508-561-7553	
ENERGY RETROFIT AND ELECTRIFICATION 13 Rice Spring Lane Wayland, MA 01778	
HVAC FIRST FLOOR	
10-10-2025	H-4 4 of 5